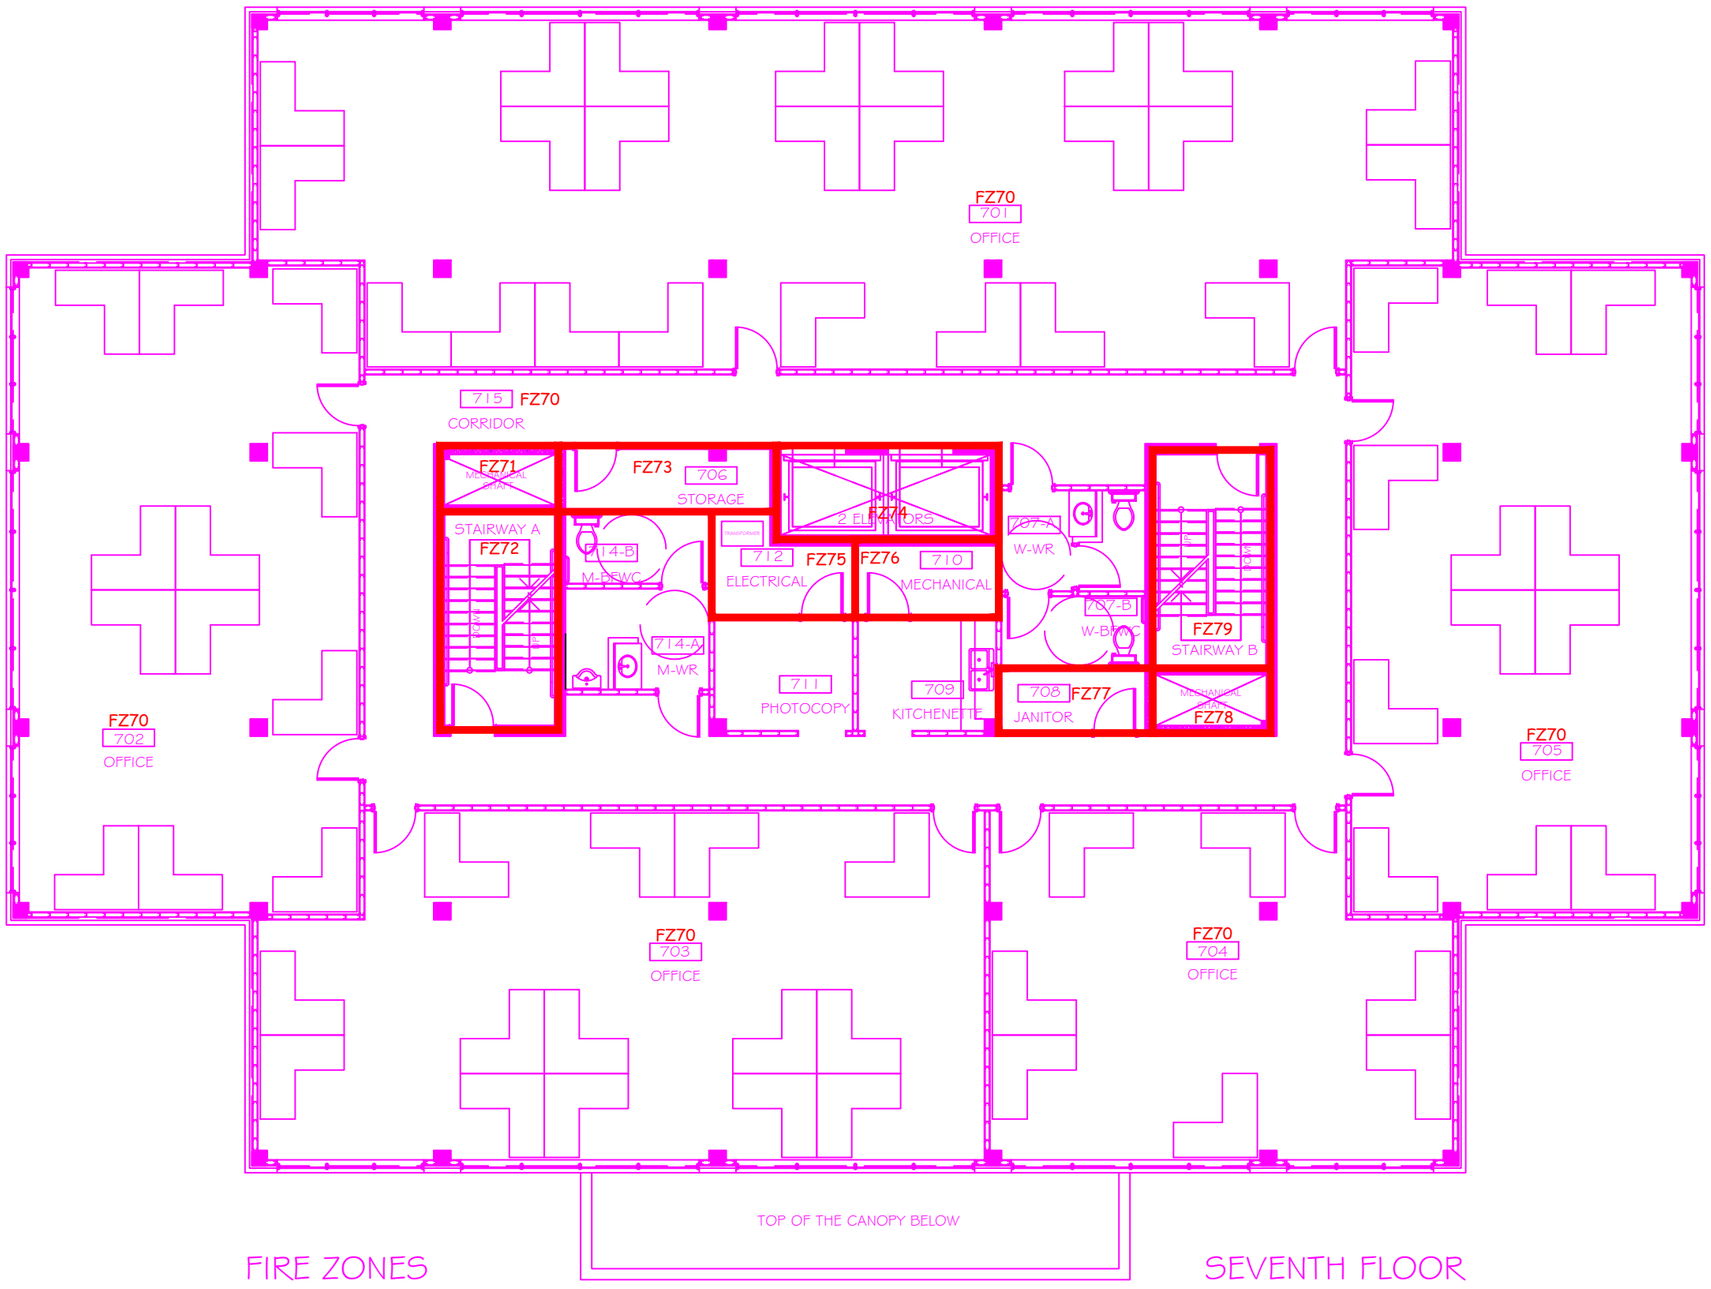

FIRE ZONES SEVENTH FLOOR

FIRE ZONES LEGEND:

FZ70	OFFICES & CENTRAL CORE: 707-A/B, 709,711 & 714-A/B
FZ71	WEST MECHANICAL SHAFT
FZ72	STAIRWAY A
FZ73	STORAGE 706
FZ74	ELEVATORS
FZ75	ELECTRICAL 712
FZ76	MECHANICAL 710
FZ77	JANITOR 708
FZ78	EAST MECHANICAL SHAFT
FZ79	STAIRWAY B

ALGONQUIN COLLEGE

ELECTRICAL DESIGN WITH AUTOCAD

COURSE NUMBER: ELE8944

COURSE SECTION: 030

TITLE: COMMERCIAL BUILDING ELECTRICAL DESIGN FIRE ZONE PLAN

PROJECT: PROJECT #2

DATE: 2023-12-11

STUDENT NAME: HURUY HURUY

DRAWING SCALE: 1 :130

REVISION NUMBER/DATE: #01: 2023-12-03

DRAWING NUMBER E07